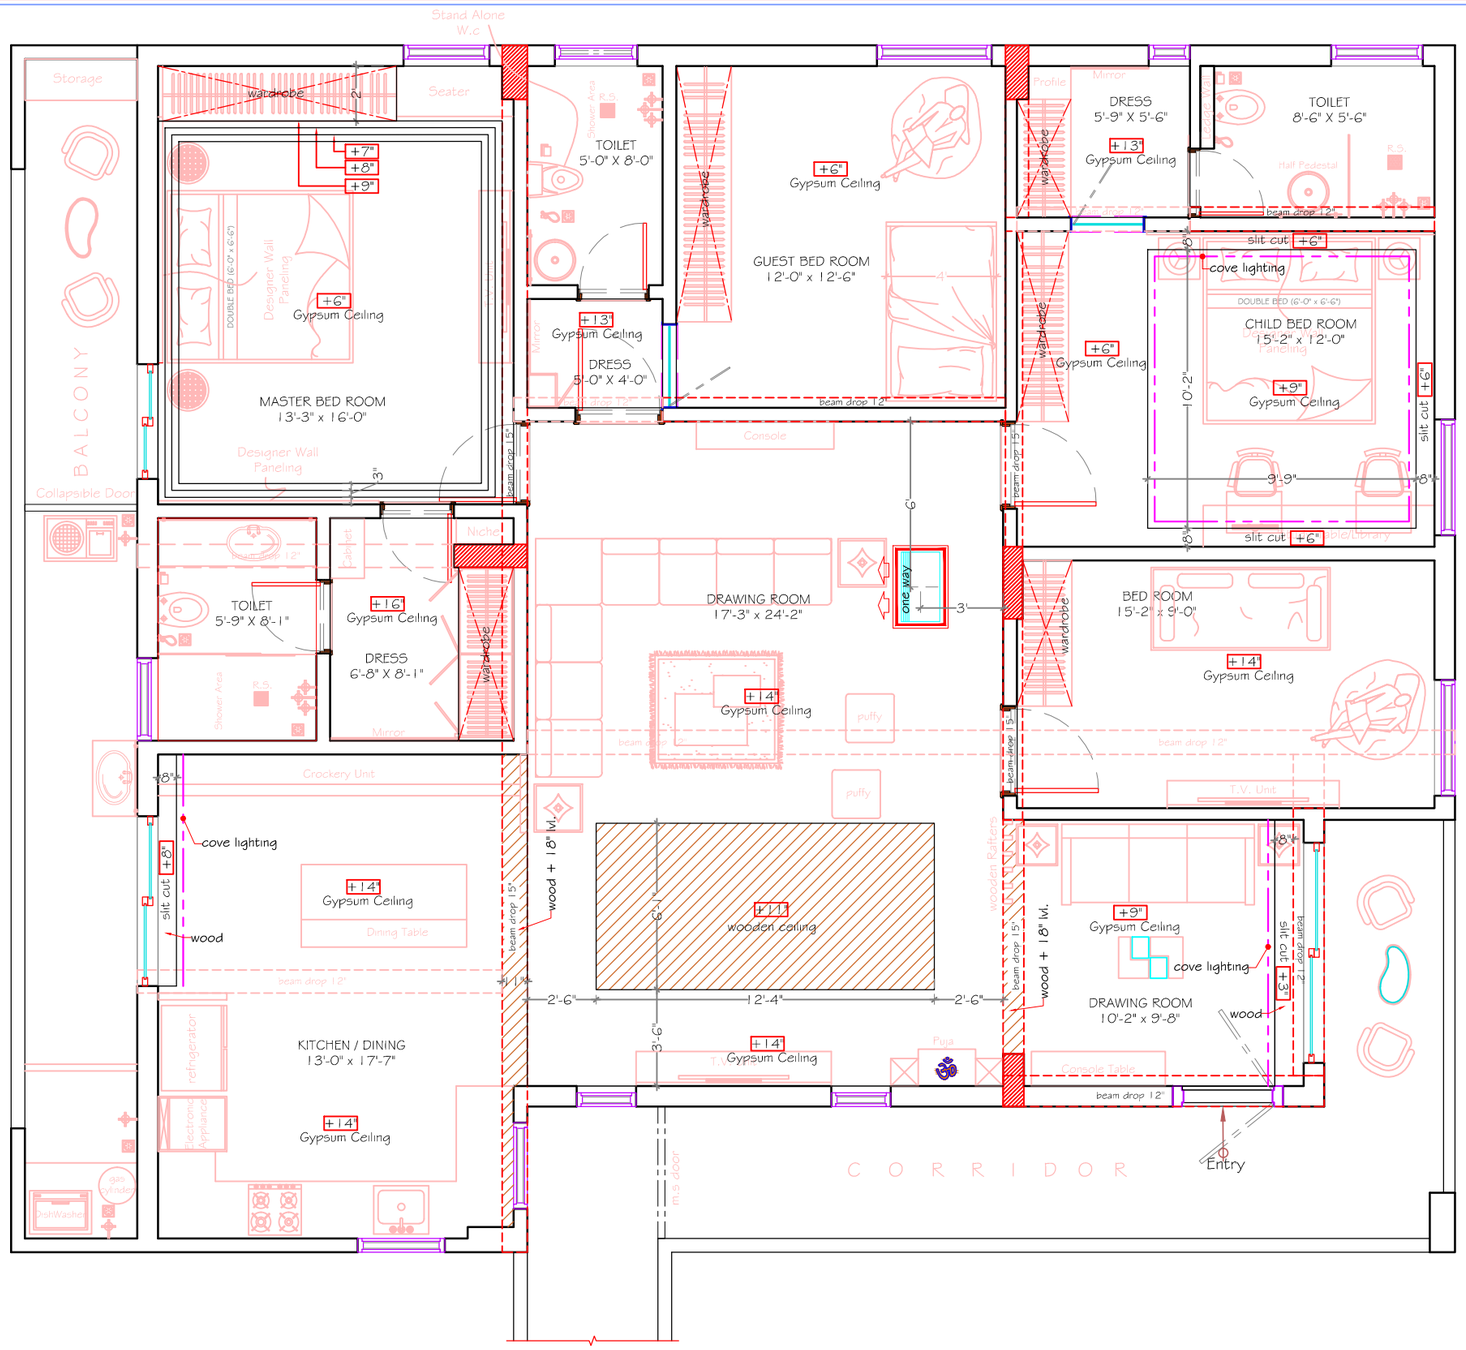

N Square

HAS THE COPY RIGHTS OF THIS DOCUMENT, AND IT SHOULDN'T BE USED BY ANYBODY WITHOUT THEIR PERMISSION ***

GENERAL NOTE

1. all dimensions are in feet and inches unless specified.
2. don't scale this drawing, only written dimensions are to be followed

CLIENT :- MR.KANCHAN THAKUR

PROJECT :- PROPOSED FLAT INTERIORS @ LAKDI KA PUL

TITLE :- FALSE CEILING DETAILS

DEALT	: MOHD SALMAN
CHECKED	: VARUN JAIN
DATE	: 04-11-2020
SCALE	: N.T.S.

DWG. : 01

W S N E

N.SQUARE
VARUN JAIN
PH.NO. 040-66559885